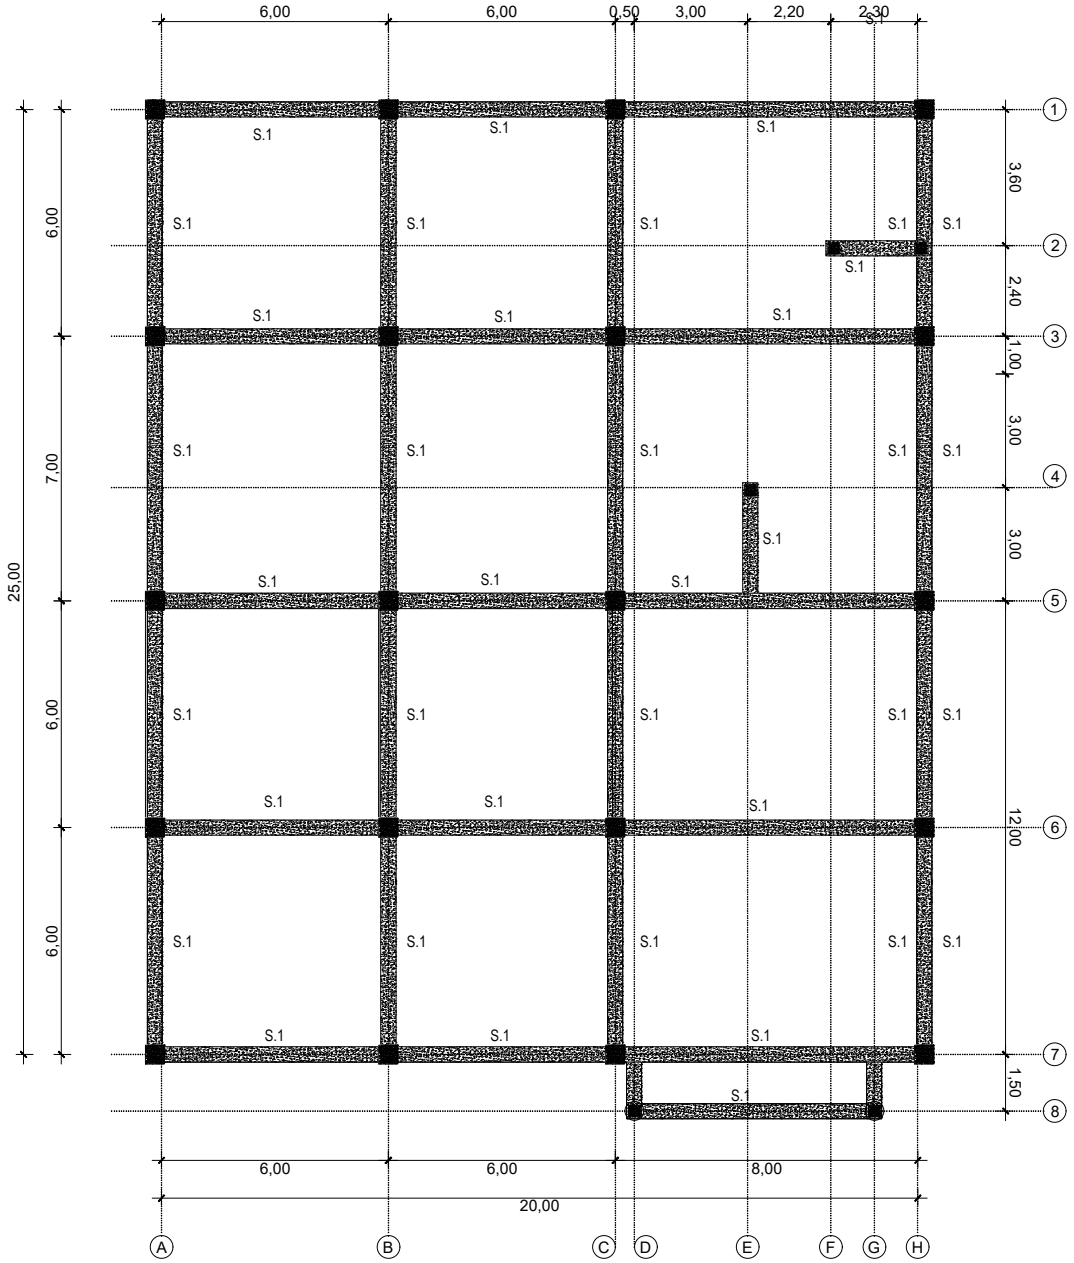


TIPE SLOOF	DIMENSI		POTONGAN	
	ℓ	t	TUMPUAN	LAPANGAN
S.1	40	60	0,60 / 0,40 — 1:25	0,60 / 0,40 — 1:25
TULANGAN ATAS			4 D22	4 D22
TULANGAN TENGAH			2 D12	2 D12
TULANGAN BAWAH			4 D22	4 D22
TULANGAN SENGKANG			Ø10 - 100	Ø10 - 150
TEBAL SELIMUT BETON			5 cm	5 cm

STR 2. **DENAH SLOOF**

Skala 1 : 200

UNIVERSITAS TIDAR

JL. KAPTEN SUPARMAN 39 POTROBANGSAN,MAGELANG UTARA, JAWA TENGAH 56116

NAMA BANGUNAN

UNTIDAR STUDY CENTER (USC)

JUDUL GAMBAR

DENAH SLOOF

DIGAMBAR OLEH :

KELOMPOK 16/ TS 03

Muh. Bima Adjie (2505030078)
Ivana Syahda W (2505030100)

DISETUJUI OLEH :

Ir. Muhammad Amin ST. MT. IPM.

Marsha Cahyati

SKALA

1 : 200

NOMOR GAMBAR

16

JUMLAH GAMBAR

80